
RUMAH 10902

PAKET GAMBAR RENCANA

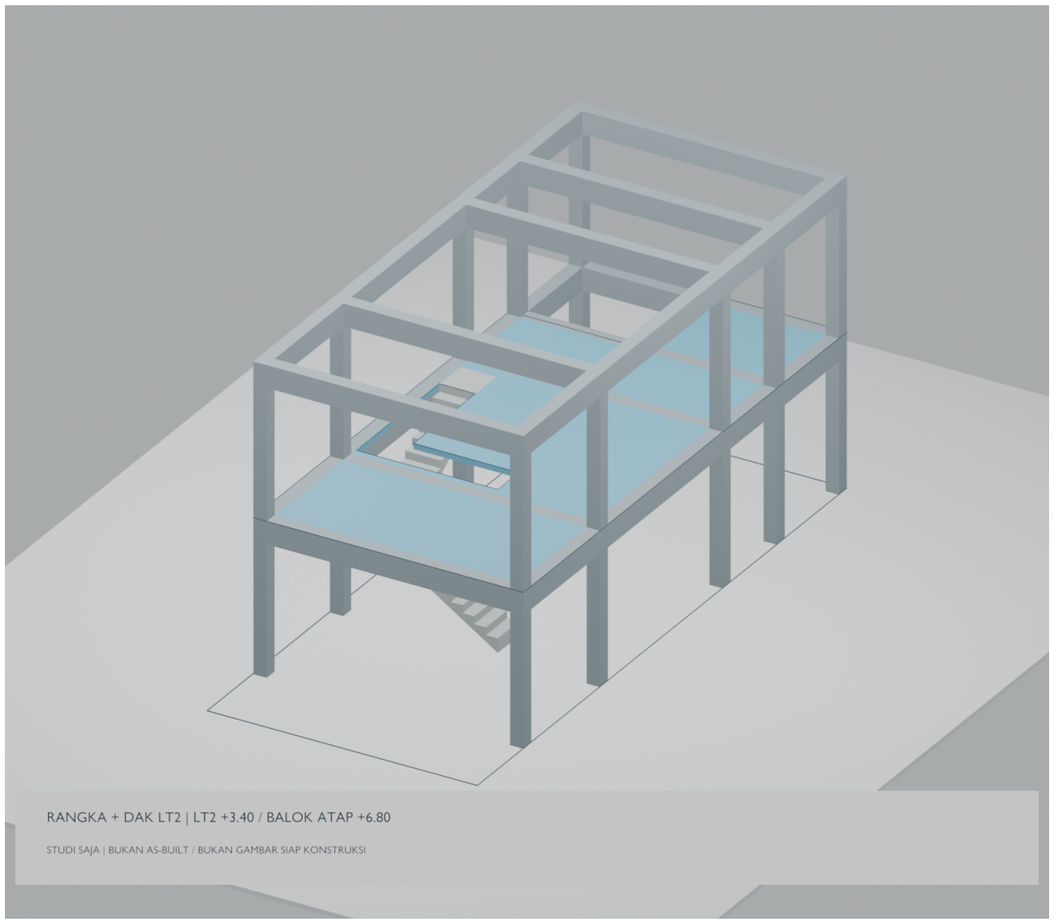

BUKAN AS-BUILT - BELUM DIPERIKSA PERENCANA STRUKTUR

27 OKTOBER 2026 | 12 LEMBAR A3 | DATA DAN ASUMSI DIBEDAKAN

Tidak untuk pengecoran, fabrikasi besi atau penetapan pondasi.

DAFTAR GAMBAR

KODE	NAMA LEMBAR
G-00	Sampul dan status paket
G-01	Daftar gambar, datum, legenda dan status data
A-01	Denah LT1 - acuan tinggi baru
A-02	Denah LT2 - opsi revisi tangga dan dua pintu sejajar
A-03	Potongan A-A / B-B dan elevasi
S-01	Denah titik pondasi dan kolom
S-02	Denah balok LT2 +3.400
S-03	Denah balok atap +6.800 / opsi dak
S-04	Denah pelat LT2 dan tangga
S-05	Penampang studi dan tabel status tulangan
Q-01	Rekap volume / allowance besi dan batas hitungan
V-01	Isometri rangka, pelat dan tulangan ilustratif

DATUM / GRID

SUMBU	KOORDINAT mm
A / B	150 / 5850
1	1900
2	4800
3	9450
4	11500
5	13850

O=(0,0,0). X melintang; Y depan ke belakang; Z ke atas. Batas tapak konsep 6000 x 14000 mm.

LT1 +0; LT2 +3400; bawah balok +2900 / +6300; atas balok atap +6800. Plafon target +2800 / +6200.

JENIS DATA	STATUS
GEOMETRI	Skenario P01 berbasis RevCB; bukan survei. Denah LT2 direvisi untuk tangga.
UKURAN STRUKTUR	Envelope studi K1 300x300, B1/RB 300x500, pelat 120; belum pembuktian kapasitas.
PONDASI / BESI	Jenis, kedalaman, ukuran telapak/tiang, mutu, jumlah/diameter tulangan belum ditetapkan.
MODEL 3D	Pola batang visual; bukan BBS, bukan detail sambungan/penyaluran.
CETAK	Skala berlaku pada A3 100%. Isometri dan diagram diberi NTS.

PEMILIK / PROYEK

RUMAH 10902

NAMA PEKERJAAN

PAKET GAMBAR RENCANA RUMAH DUA LANTAI

ALAMAT / TAPAK

Babat Jerawat, Surabaya (acuan dokumen; bukan survei)

DASAR GAMBAR

Master RevCB; skenario tinggi LT2 +3400 / atas balok atap +6800 mm.

DIGAMBAR

Studi berbantuan model. Bukan tanda tangan/pernyataan perencana.

DIPERIKSA

BELUM DIPERIKSA PERENCANA STRUKTUR

STATUS DOKUMEN

RENCANA / STUDI

BUKAN AS-BUILT

DAFTAR GAMBAR, DATUM DAN STATUS DATA

KODE: G-01

SKALA: NTS | A3

LEMBAR 02 / 12

UNIT: mm | CETAK 100%

P01 | 27 OKTOBER 2026

Tidak untuk pelaksanaan konstruksi.

DATUM


LT1 +0 / LT2 +3400. Unit dimensi mm.

BATAS LAHAN

6000 x 14000 adalah asumsi denah. Tidak mengubah batas pada dokumen tanah.

BUKAAN

Tidak ada bukaan ke tetangga kanan-kiri. Bukaan taman menghadap lahan sendiri.

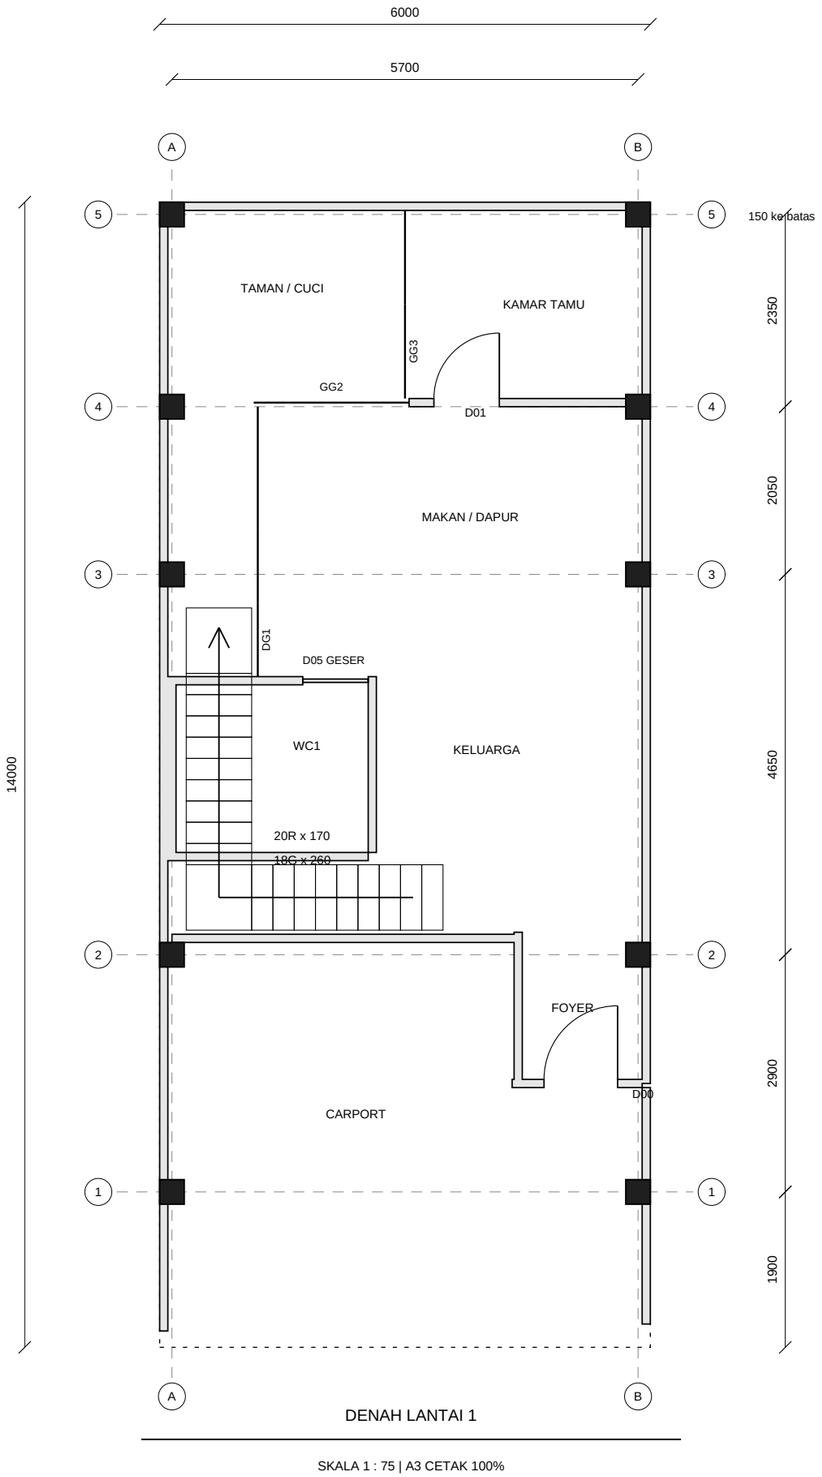

DENAH LANTAI 1

SKALA 1 : 75 | A3 CETAK 100%

ACUAN LT1

Garis dinding dari section final RevCB. Posisi tangga diperbarui pada lembar ini. WC berada di bawah sebagian flight; ruang kepala belum disahkan.

PINTU	KETERANGAN
D00	Pintu masuk depan, nominal 900
D01	Kamar tamu, nominal 800
D05	WC1 geser, nominal 800
D07/D08	Dua kamar LT2, nominal 800
D09	WC2 dari hall, nominal 800
D11/D12	Master / akses balkon

Nominal bukan lebar bersih kusen. J01-J03: kaca LT2; DG1/GG2/GG3: kaca taman LT1; D12: balkon. Kolom dan furnitur belum dikoordinasikan menjadi ukuran bersih final.

PEMILIK / PROYEK

RUMAH 10902

NAMA PEKERJAAN

PAKET GAMBAR RENCANA RUMAH DUA LANTAI

ALAMAT / TAPAK

Babat Jerawat, Surabaya (acuan dokumen; bukan survei)

DASAR GAMBAR

Master RevCB; skenario tinggi LT2 +3400 / atas balok atap +6800 mm.

DIGAMBAR

Studi berbantuan model. Bukan tanda tangan/pernyataan perencana.

DIPERIKSA

BELUM DIPERIKSA PERENCANA STRUKTUR

STATUS DOKUMEN

RENCANA / STUDI

BUKAN AS-BUILT

DENAH LT1 / SKENARIO TINGGI BARU

KODE: A-01

SKALA: 1 : 75 | A3

LEMBAR 03 / 12

UNIT: mm | CETAK 100%

P01 | 27 OKTOBER 2026

Tidak untuk pelaksanaan konstruksi.

DATUM


LT1 +0 / LT2 +3400. Unit dimensi mm.

BATAS LAHAN

6000 x 14000 adalah asumsi denah. Tidak mengubah batas pada dokumen tanah.

BUKAAN

Tidak ada bukaan ke tetangga kanan-kiri. Bukaan taman menghadap lahan sendiri.

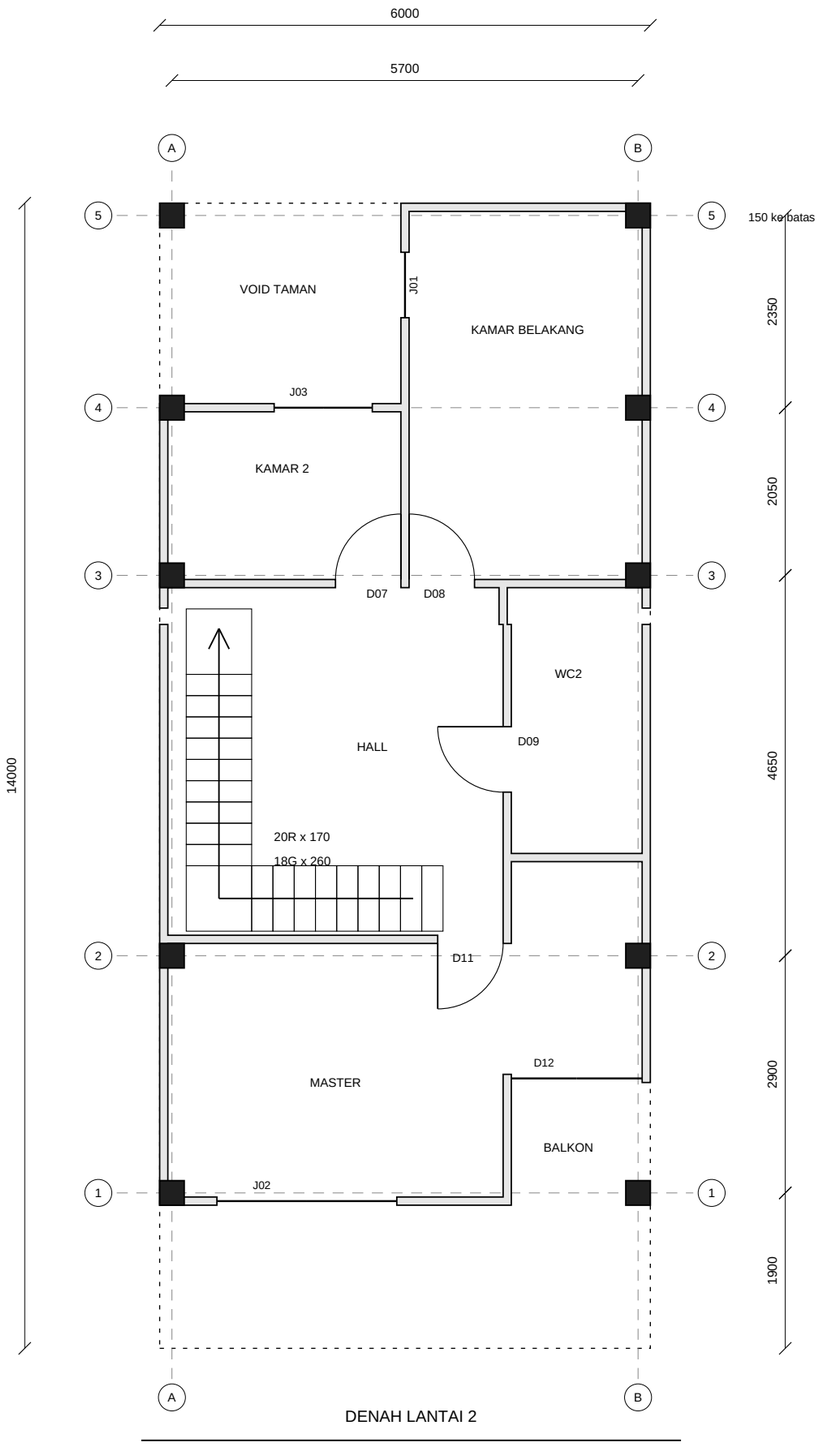

DENAH LANTAI 2

SKALA 1 : 75 | A3 CETAK 100%

REVISI LT2

Batas depan dua kamar belakang pada Y=9300-9400. Pintu D07-D08 sejajar pada Y=9400. Ini usulan perubahan, belum master arsitektur final.

Tangga 20R x170; lebar 800. Bordes atas Y8240-9040. Kamar 2 menjadi lebih dangkal; ranjang/lemari dan WC perlu koordinasi ulang.

PINTU	KETERANGAN
D00	Pintu masuk depan, nominal 900
D01	Kamar tamu, nominal 800
D05	WC1 geser, nominal 800
D07/D08	Dua kamar LT2, nominal 800
D09	WC2 dari hall, nominal 800
D11/D12	Master / akses balkon

Nominal bukan lebar bersih kusen. J01-J03: kaca LT2; DG1/GG2/GG3: kaca taman LT1; D12: balkon. Kolom dan furnitur belum dikoordinasikan menjadi ukuran bersih final.

PEMILIK / PROYEK

RUMAH 10902

NAMA PEKERJAAN

PAKET GAMBAR RENCANA RUMAH DUA LANTAI

ALAMAT / TAPAK

Babat Jerawat, Surabaya (acuan dokumen; bukan survei)

DASAR GAMBAR

Master RevCB; skenario tinggi LT2 +3400 / atas balok atap +6800 mm.

DIGAMBAR

Studi berbantuan model. Bukan tanda tangan/pernyataan perencana.

DIPERIKSA

BELUM DIPERIKSA PERENCANA STRUKTUR

STATUS DOKUMEN

RENCANA / STUDI

BUKAN AS-BUILT

DENAH LT2 / SKENARIO TINGGI BARU

KODE: A-02

SKALA: 1 : 75 | A3


LEMBAR 04 / 12

UNIT: mm | CETAK 100%

P01 | 27 OKTOBER 2026


Tidak untuk pelaksanaan konstruksi.

A-A | X=725 mm

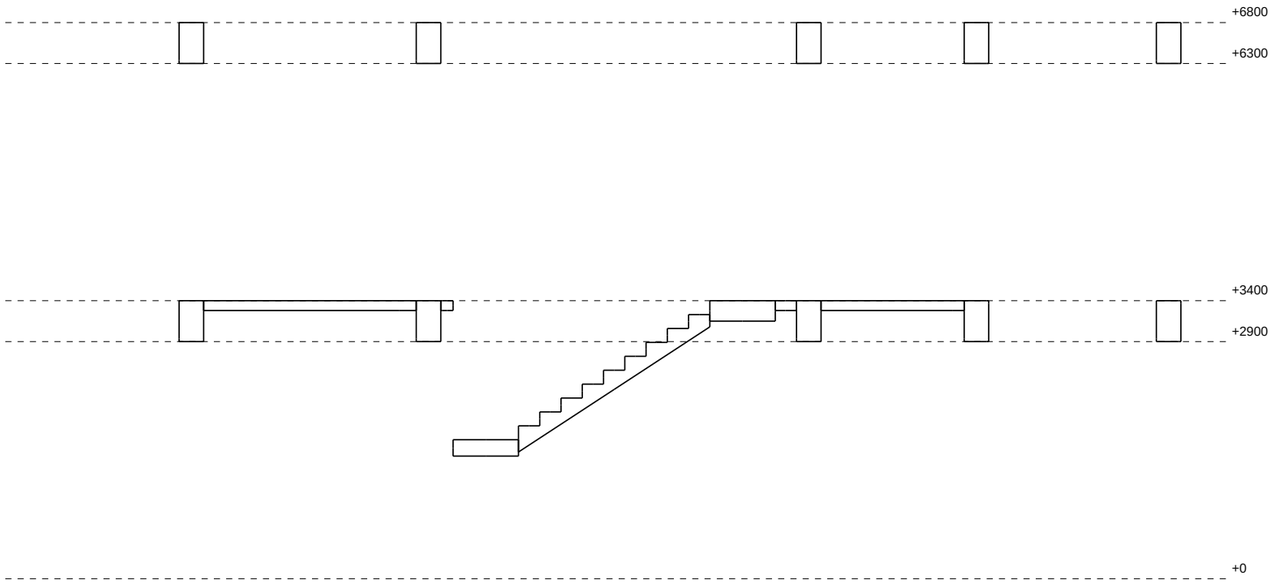

POTONGAN MEMANJANG / 1 : 75

B-B | Y=4800 mm

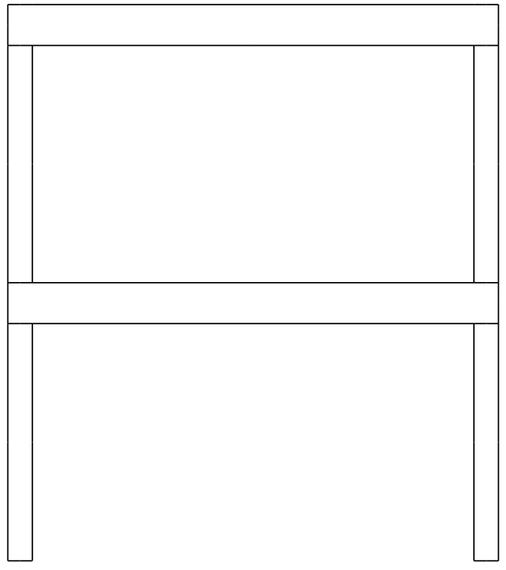

MELINTANG / 1 : 75

ELEVASI	ACUAN	STATUS
LT1 / LT2	+0 / +3400	Konsep, bukan elevasi patok
Plafon target	+2800 / +6200	Ruang bersih target 2800
Atas balok atap	+6800	Atap ringan default; bukan pelat atap
Puncak atap	Belum dikunci	Parapet / ventilator belum dikoordinasikan

Potongan diambil dari mesh beton P01 yang sama dengan Blender. Bukan detail sambungan. Sisi, finishing, railing, ruang kepala WC dan seluruh lintasan duct belum diuji lengkap.

PEMILIK / PROYEK

RUMAH 10902

NAMA PEKERJAAN

PAKET GAMBAR RENCANA RUMAH DUA LANTAI

ALAMAT / TAPAK

Babat Jerawat, Surabaya (acuan dokumen; bukan survei)

DASAR GAMBAR

Master RevCB; skenario tinggi LT2 +3400 / atas balok atap +6800 mm.

DIGAMBAR

Studi berbantuan model. Bukan tanda tangan/pernyataan perencana.

DIPERIKSA

BELUM DIPERIKSA PERENCANA STRUKTUR

STATUS DOKUMEN

RENCANA / STUDI

BUKAN AS-BUILT

POTONGAN STRUKTUR A-A / B-B

KODE: A-03

SKALA: 1 : 75 | A3

LEMBAR 05 / 12

UNIT: mm | CETAK 100%

P01 | 27 OKTOBER 2026

Tidak untuk pelaksanaan konstruksi.

K1


10 posisi kolom; 20 segmen antara zona balok dalam model.

P-A1 s/d P-B5

Lingkaran adalah titik tumpuan, BUKAN ukuran telapak.

DATA TANAH

Belum tersedia. Tidak ada SPT, daya dukung, kedalaman atau ukuran tiang yang dikarang.

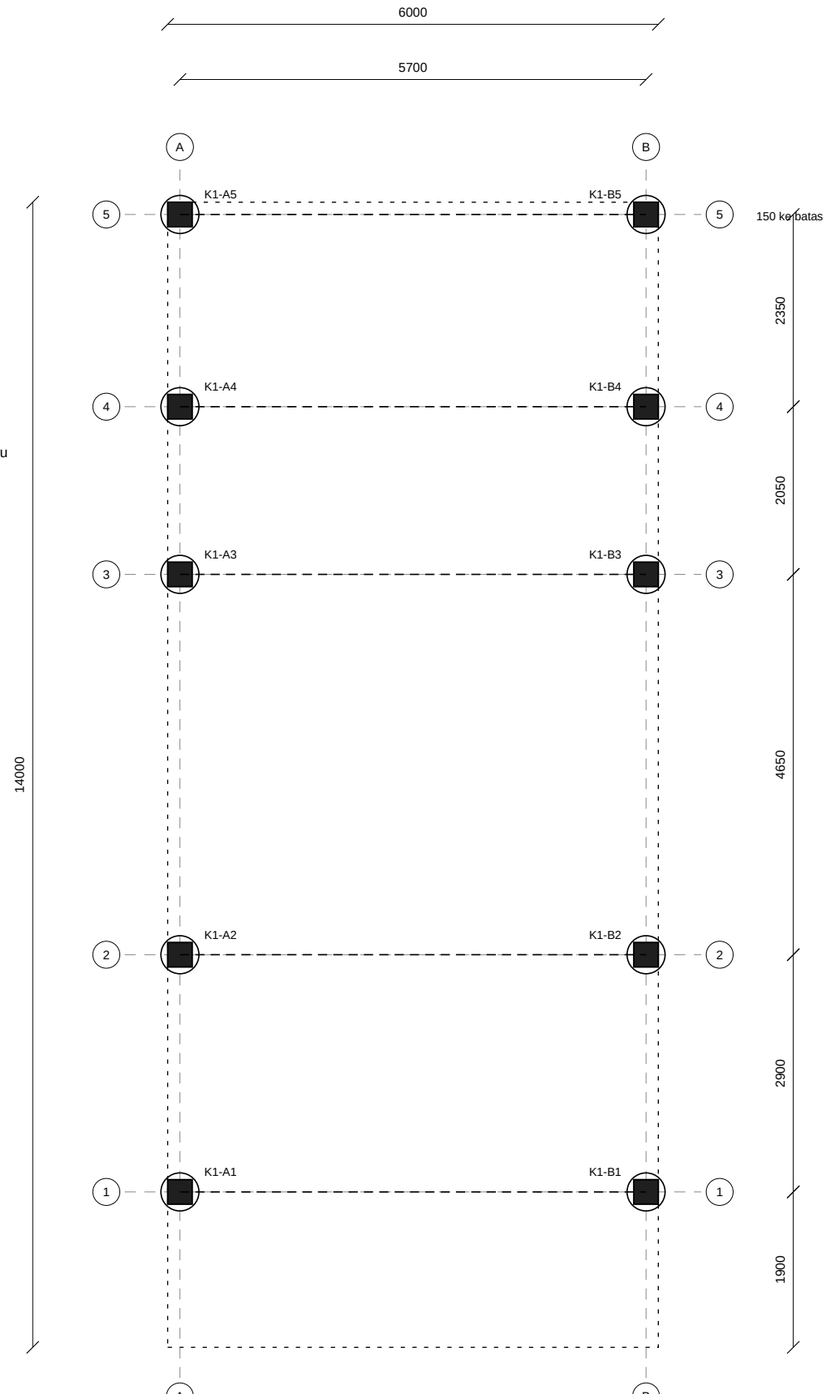

TITIK PONDASI DAN KOLOM

SKALA 1 : 75 | A3 CETAK 100%

KODE	KETERANGAN
K1	Kolom 300x300 mm (studi)
P	Pondasi belum dipilih/didesain
Putus	Jalur studi strap/pengikat; ukuran dan tulangan belum ditentukan

Semua tapak pondasi harus berada pada lahan sendiri. Kolom dekat batas menghasilkan eksentrisitas; jangan menggambar telapak sentris melewati lahan tetangga.

Opsi: telapak eksentris dengan strap/gabungan jika tanah memenuhi. Jika tidak, pilih sistem yang sesuai hasil geoteknik. Garis ini bukan spesifikasi sloof kecil biasa.

Ukuran lebar/panjang/tebal/kedalaman, jumlah tiang dan tulangan: BELUM DITETAPKAN. Rekap Q-01 tidak termasuk pondasi.

PEMILIK / PROYEK

RUMAH 10902

NAMA PEKERJAAN

PAKET GAMBAR RENCANA RUMAH DUA LANTAI

ALAMAT / TAPAK

Babat Jerawat, Surabaya (acuan dokumen; bukan survei)

DASAR GAMBAR

Master RevCB; skenario tinggi LT2 +3400 / atas balok atap +6800 mm.

DIGAMBAR

Studi berbantuan model. Bukan tanda tangan/pernyataan perencana.

DIPERIKSA

BELUM DIPERIKSA PERENCANA STRUKTUR

STATUS DOKUMEN

RENCANA / STUDI

BUKAN AS-BUILT

DENAH TITIK PONDASI DAN KOLOM

KODE: S-01

SKALA: 1 : 75 | A3

LEMBAR 06 / 12

UNIT: mm | CETAK 100%

P01 | 27 OKTOBER 2026

Tidak untuk pelaksanaan konstruksi.

ENVELOPE


B1 300x500 mm. Bukan hasil desain kapasitas.

ELEVASI

Atas +3400; bawah +2900 mm.

TULANGAN

Diameter, jumlah, jarak sengkang dan sambungan belum ditetapkan.

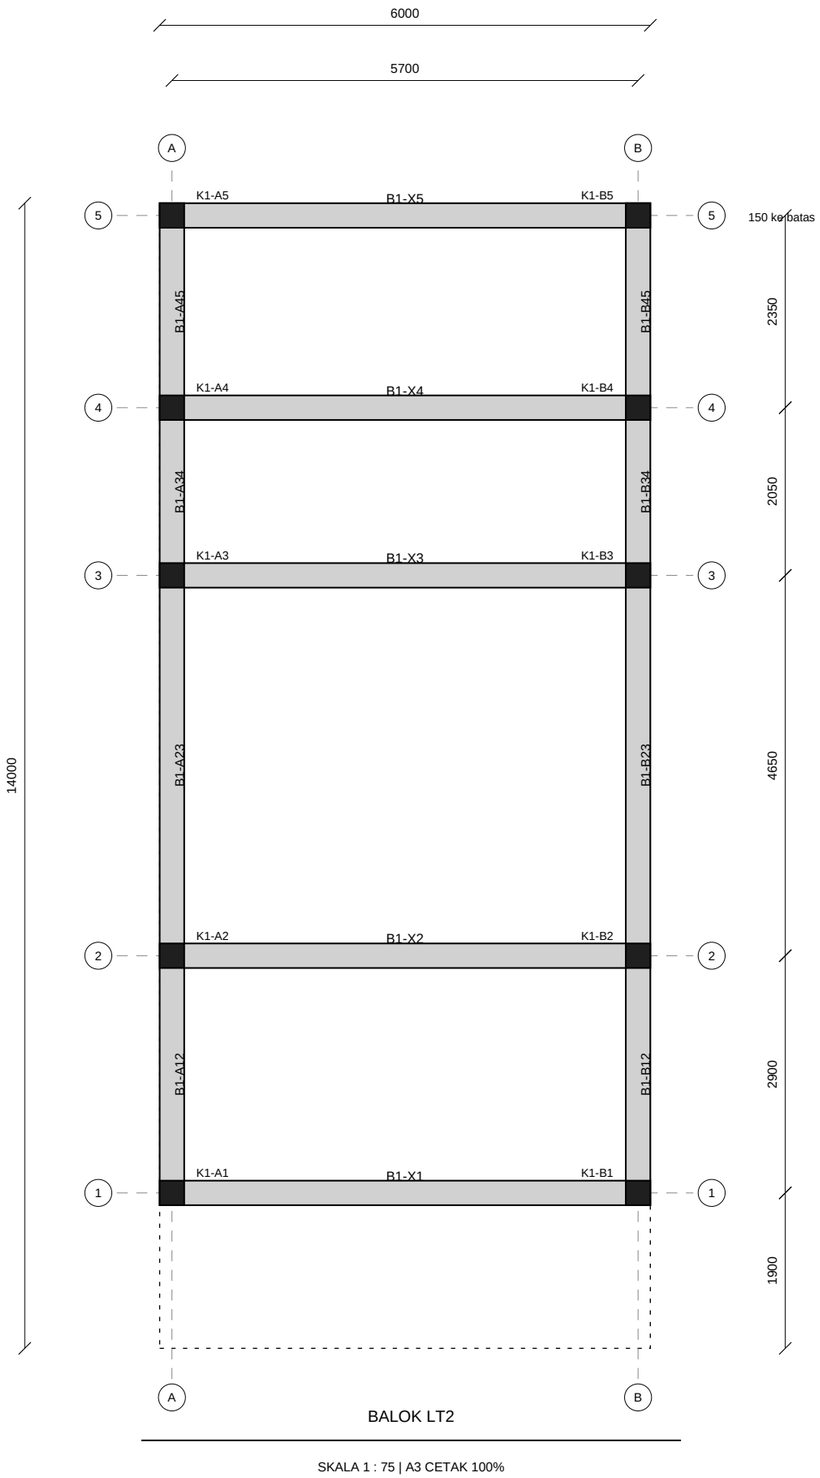

BALOK LT2

SKALA 1 : 75 | A3 CETAK 100%

ANGGOTA	BENTANG SUMBU mm
B1-X1	5700
B1-X2	5700
B1-X3	5700
B1-X4	5700
B1-X5	5700
B1-A12	2900
B1-A23	4650
B1-A34	2050
B1-A45	2350
B1-B12	2900
B1-B23	4650
B1-B34	2050
B1-B45	2350

13 garis anggota per tingkat; balok beton dimodelkan sebagai union agar volume simpul tidak dihitung berulang. Bentang sumbu bukan panjang potong besi.

Balok tepi tangga dan kaca taman perlu koordinasi. Tidak ada izin membuat lubang duct pada balok tanpa desain.

PEMILIK / PROYEK

RUMAH 10902

NAMA PEKERJAAN

PAKET GAMBAR RENCANA RUMAH DUA LANTAI

ALAMAT / TAPAK

Babat Jerawat, Surabaya (acuan dokumen; bukan survei)

DASAR GAMBAR

Master RevCB; skenario tinggi LT2 +3400 / atas balok atap +6800 mm.

DIGAMBAR

Studi berbantuan model. Bukan tanda tangan/pernyataan perencana.

DIPERIKSA

BELUM DIPERIKSA PERENCANA STRUKTUR

STATUS DOKUMEN

RENCANA / STUDI

BUKAN AS-BUILT

DENAH BALOK LT2 +3400

KODE: S-02

SKALA: 1 : 75 | A3

LEMBAR 07 / 12

UNIT: mm | CETAK 100%

P01 | 27 OKTOBER 2026

Tidak untuk pelaksanaan konstruksi.

ENVELOPE


RB 300x500 mm. Bukan hasil desain kapasitas.

ELEVASI

Atas +6800; bawah +6300 mm.

TULANGAN

Diameter, jumlah, jarak sengkang dan sambungan belum ditetapkan.

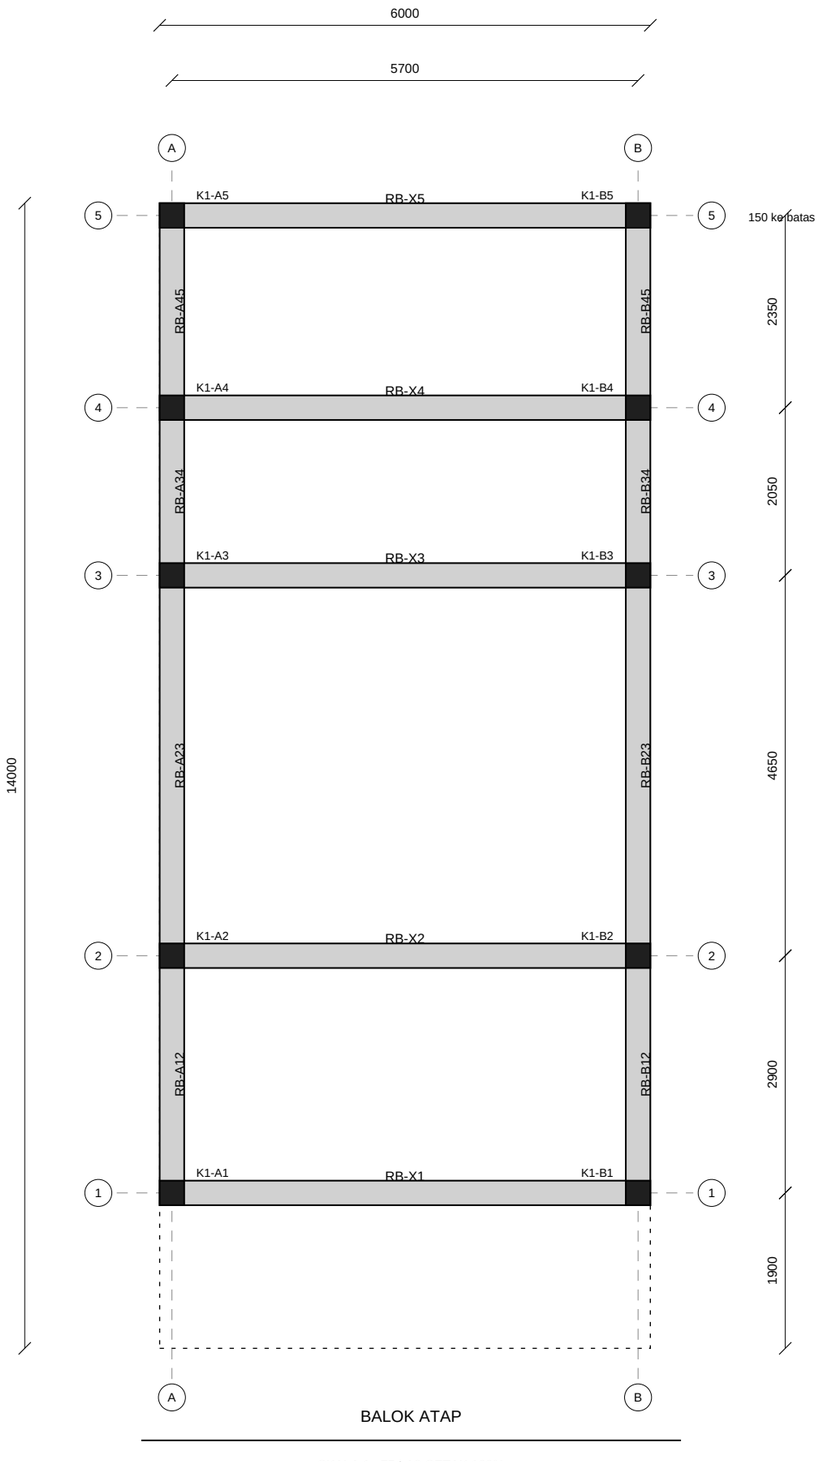

BALOK ATAP

SKALA 1 : 75 | A3 CETAK 100%

ANGGOTA	BENTANG SUMBU mm
RB-X1	5700
RB-X2	5700
RB-X3	5700
RB-X4	5700
RB-X5	5700
RB-A12	2900
RB-A23	4650
RB-A34	2050
RB-A45	2350
RB-B12	2900
RB-B23	4650
RB-B34	2050
RB-B45	2350

13 garis anggota per tingkat; balok beton dimodelkan sebagai union agar volume simpul tidak dihitung berulang. Bentang sumbu bukan panjang potong besi.

Atap ringan adalah asumsi default. Dak atap beton adalah opsi NONAKTIF pada scene utama; tambahan berat belum dianalisis.

PEMILIK / PROYEK

RUMAH 10902

NAMA PEKERJAAN

PAKET GAMBAR RENCANA RUMAH DUA LANTAI

ALAMAT / TAPAK

Babat Jerawat, Surabaya (acuan dokumen; bukan survei)

DASAR GAMBAR

Master RevCB; skenario tinggi LT2 +3400 / atas balok atap +6800 mm.

DIGAMBAR

Studi berbantuan model. Bukan tanda tangan/pernyataan perencana.

DIPERIKSA

BELUM DIPERIKSA PERENCANA STRUKTUR

STATUS DOKUMEN

RENCANA / STUDI

BUKAN AS-BUILT

DENAH BALOK ATAP +6800

KODE: S-03

SKALA: 1 : 75 | A3

LEMBAR 08 / 12

UNIT: mm | CETAK 100%

P01 | 27 OKTOBER 2026

Tidak untuk pelaksanaan konstruksi.

PL1


Luas lantai termasuk bidang di atas balok: 61,466 m2. Pelat bersih model di luar balok/bordes dicatat pada Q-01.

BUKAAN TANGGA

4,384 m2 untuk dua flight; bordes atas menjadi bagian lantai.

STATUS


Tebal pelat dan bordes belum dibuktikan terhadap lendutan, punching atau kekuatan.

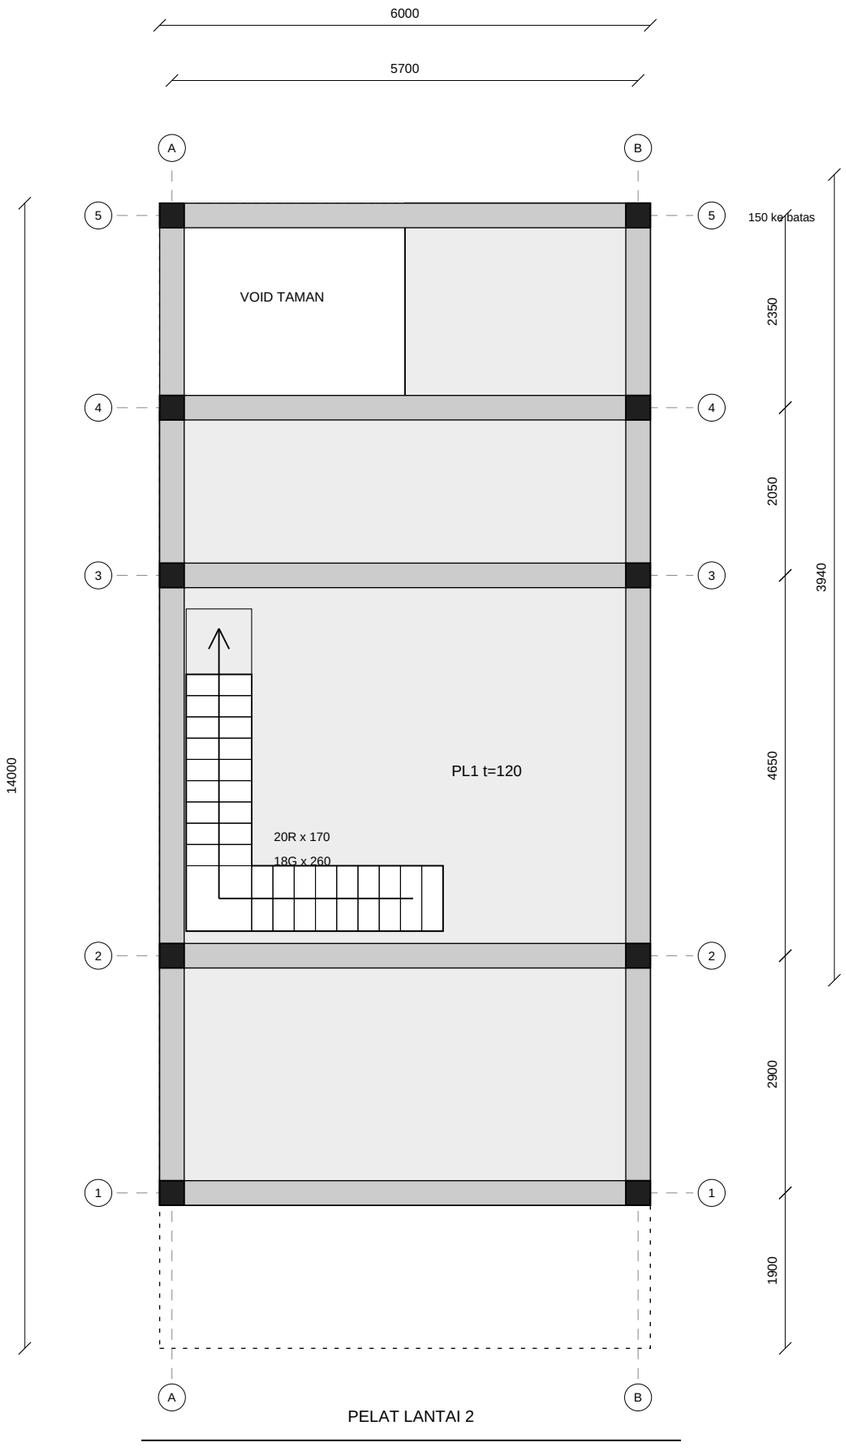

PELAT LANTAI 2

SKALA 1 : 75 | A3 CETAK 100%

DETAIL TANGGA / 1 : 30

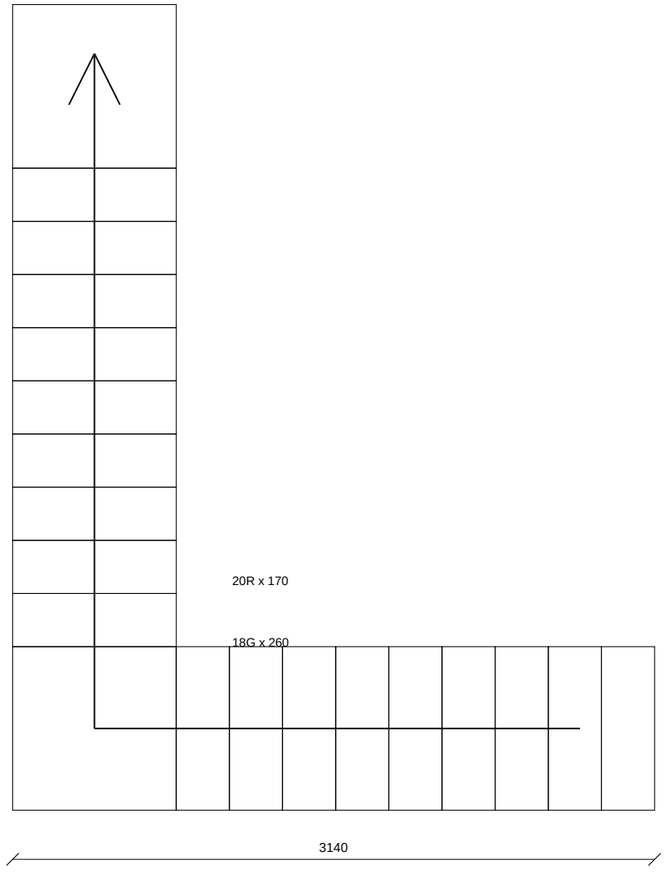

20R x170 =3400. Dua flight, 9G x260 per flight. Lebar 800; bordes 800x800. Celah sisi ke envelope balok hanya 25 mm sebelum finishing.

Bordes model: putar t=200, atas t=250 mm (visual saja). Tulangan dan tumpuan belum dirancang; bukan standar tebal bordes.

PEMILIK / PROYEK

RUMAH 10902

NAMA PEKERJAAN

PAKET GAMBAR RENCANA RUMAH DUA LANTAI

ALAMAT / TAPAK

Babat Jerawat, Surabaya (acuan dokumen; bukan survei)

DASAR GAMBAR

Master RevCB; skenario tinggi LT2 +3400 / atas balok atap +6800 mm.

DIGAMBAR

Studi berbantuan model. Bukan tanda tangan/pernyataan perencana.

DIPERIKSA

BELUM DIPERIKSA PERENCANA STRUKTUR

STATUS DOKUMEN

RENCANA / STUDI

BUKAN AS-BUILT

DENAH PELAT LT2 DAN TANGGA

KODE: S-04

SKALA: 1 : 75 / DETAIL 1 : 30 | A3


LEMBAR 09 / 12

UNIT: mm | CETAK 100%


P01 | 27 OKTOBER 2026

Tidak untuk pelaksanaan konstruksi.


K1 / 300 x 300

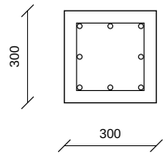

B1 / RB / 300 x 500

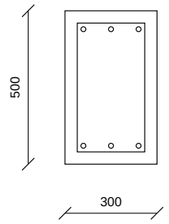

PL1 / t=120

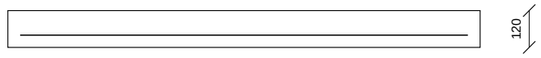


Potongan tebal 1 : 20

ITEM	K1 KOLOM	B1 / RB BALOK	PL1 / TANGGA
Ukuran envelope	300x300	300x500	Pelat 120; bordes visual 200/250
Mutu beton / baja	Belum disahkan	Belum disahkan	Belum disahkan
Tulangan utama	BELUM DIRANCANG	BELUM DIRANCANG	BELUM DIRANCANG
Sengkang / distribusi	BELUM DIRANCANG	BELUM DIRANCANG	BELUM DIRANCANG
Sambungan / penyaluran	BELUM DIRANCANG	BELUM DIRANCANG	BELUM DIRANCANG

Lingkaran/garis adalah simbol pola visual sesuai model Blender, bukan penetapan jumlah atau diameter. Tidak ada detail tulangan sekolah yang disalin.

Analisis struktur, data tanah, deformasi, gempa, tumpuan, kait, sengkang joint dan panjang sambungan harus ditetapkan sebelum dokumen ini menjadi gambar pelaksanaan.

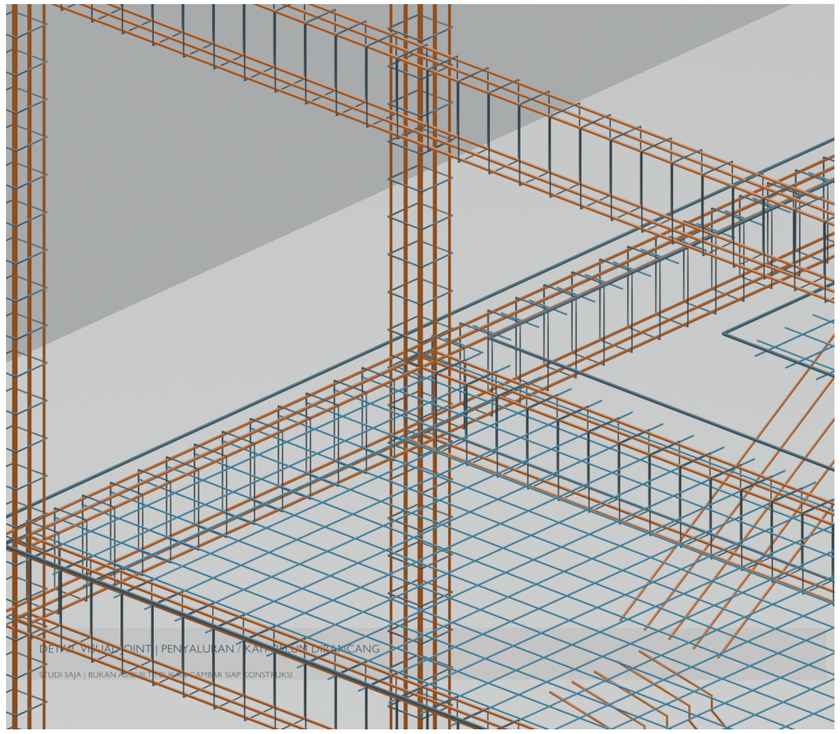

PEMILIK / PROYEK

RUMAH 10902

NAMA PEKERJAAN

PAKET GAMBAR RENCANA RUMAH DUA LANTAI

ALAMAT / TAPAK

Babat Jerawat, Surabaya (acuan dokumen; bukan survei)

DASAR GAMBAR

Master RevCB; skenario tinggi LT2 +3400 / atas balok atap +6800 mm.

DIGAMBAR

Studi berbantuan model. Bukan tanda tangan/pernyataan perencana.

DIPERIKSA

BELUM DIPERIKSA PERENCANA STRUKTUR

STATUS DOKUMEN

RENCANA / STUDI

BUKAN AS-BUILT

PENAMPANG STUDI / STATUS TULANGAN

KODE: S-05

SKALA: 1 : 20 / SIMBOL NTS | A3

LEMBAR 10 / 12

UNIT: mm | CETAK 100%

P01 | 27 OKTOBER 2026

Tidak untuk pelaksanaan konstruksi.

REKAP MODEL P01 - BUKAN BAR BENDING SCHEDULE

ELEMEN	VOL. MODEL m3	ASUMSI BESI kg/m3	ALOKASI BESI kg
Kolom	5.220	190	991.8
Balok	15.450	170	2626.5
Pelat LT2	5.699	95	541.4
Tangga / bordes	1.168	120	140.1
TOTAL	27.537	Sebelum +7%	4299.8

REKAP	NILAI / BATAS
Besi anggaran	4601 kg (~4.60 ton), termasuk allowance 7%. Bukan berat batang yang tampak pada model.
Semen anggaran	253 zak 40 kg, asumsi 350 kg/m3 +5%. Bukan resep beton; jangan ditambah lagi jika ready-mix.
Pondasi / sloof	BELUM DIHITUNG. Tidak ada diameter/ukuran/kedalaman yang dipalsukan.
Opsi dak atap	7.614 m3; beton 182.7 kN. Net vs atap ringan +144.7 kN sebelum finishing; di luar total default.
Jumlah model	10 posisi / 20 segmen kolom; 13 garis balok per tingkat; 2 flight + 2 bordes.

Volume memakai mesh tertutup yang dibuka ulang, dengan pelat dipisahkan dari bidang balok dan bordes agar tidak dihitung dua kali. Ini menggantikan perkiraan volume awal; bukan hasil desain kapasitas atau volume final RAB.

Biaya indikatif besi+semen: sekitar Rp68.7 juta (Rp11.500/kg; Rp62.500/zak), belum pondasi, agregat, upah, bekisting, angkut/bongkar dan pajak besi bila terpisah. Harga publik diperiksa 27 Oktober 2026; tidak terkunci.

Acuan harga: Riaputra Metalindo (26-10-2026) / Semesta Djaya & ASA Mandiri-Mbiz.

PEMILIK / PROYEK

RUMAH 10902

NAMA PEKERJAAN

PAKET GAMBAR RENCANA RUMAH DUA LANTAI

ALAMAT / TAPAK

Babat Jerawat, Surabaya (acuan dokumen; bukan survei)

DASAR GAMBAR

Master RevCB; skenario tinggi LT2 +3400 / atas balok atap +6800 mm.

DIGAMBAR

Studi berbantuan model. Bukan tanda tangan/pernyataan perencana.

DIPERIKSA

BELUM DIPERIKSA PERENCANA STRUKTUR

STATUS DOKUMEN

RENCANA / STUDI

BUKAN AS-BUILT

REKAP GEOMETRI DAN ALLOWANCE MATERIAL

KODE: Q-01

SKALA: NTS | A3


LEMBAR 11 / 12

UNIT: mm | CETAK 100%


P01 | 27 OKTOBER 2026

Tidak untuk pelaksanaan konstruksi.

BETON / PELAT LT2

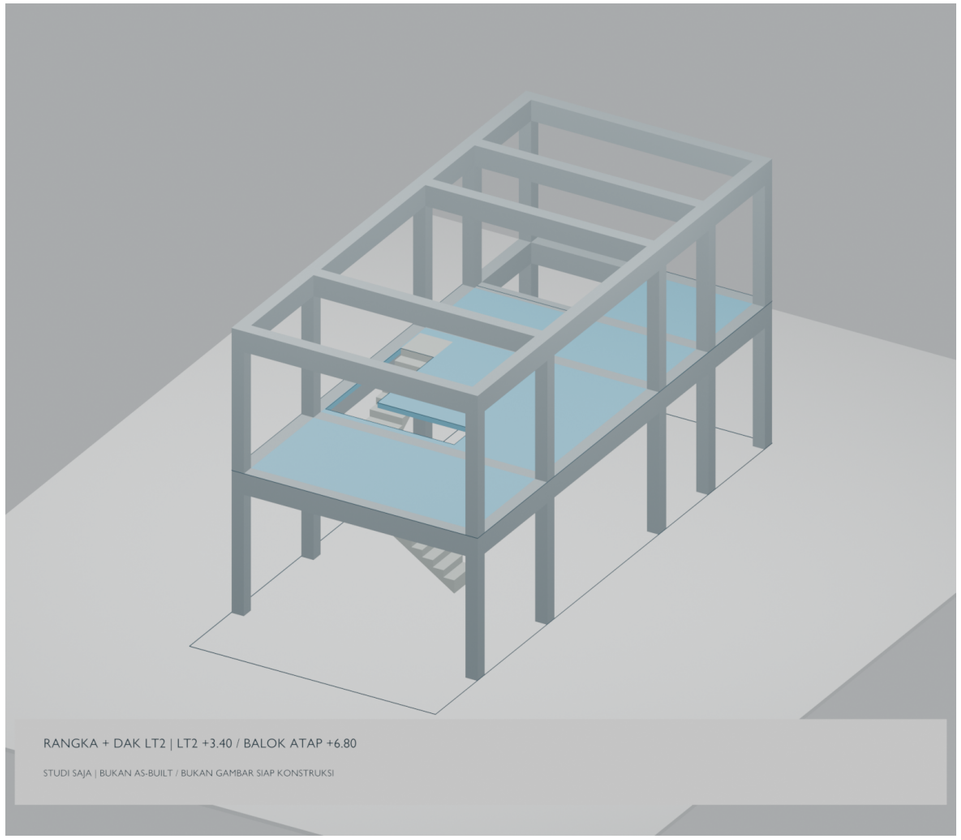

TULANGAN ILUSTRATIF

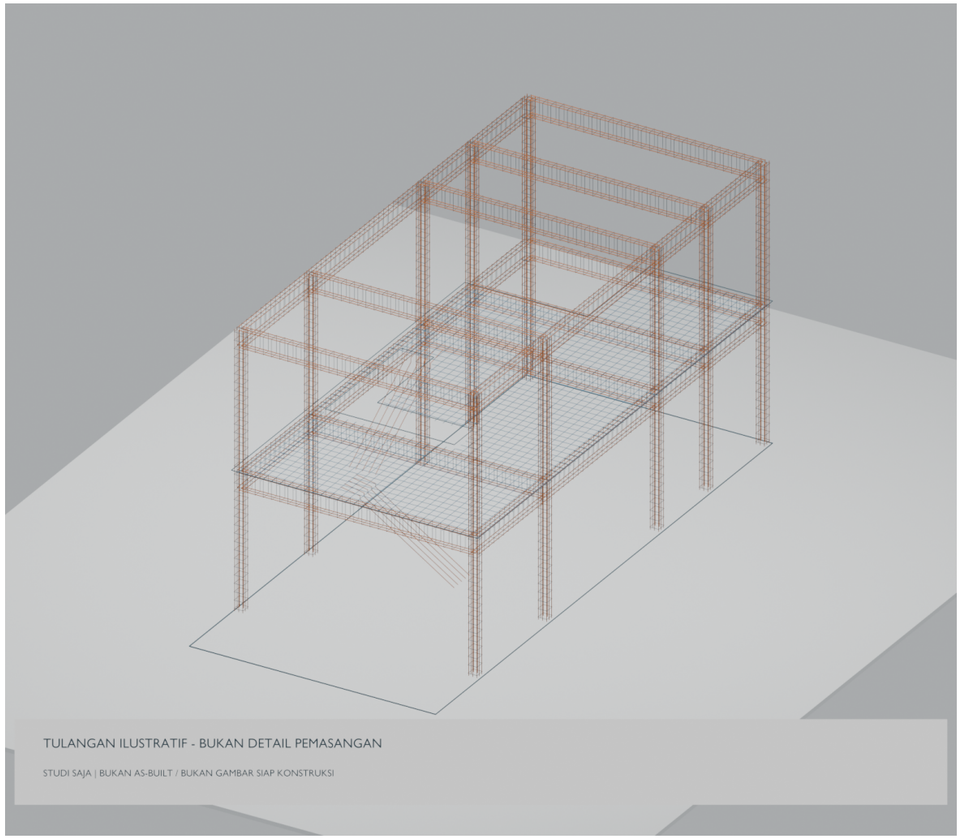

SCENE BLENDER	PENGGUNAAN
01_Rangka_Dak_LT2	Beton dan pelat lantai 2; default atap ringan tidak dimodelkan sebagai dak.
02 / 03 Tulangan	Pola batang visual, detail joint ilustratif. Bukan desain angkur, kait, sambungan atau BBS.
04_Dak_Atap_OPSI	Opsi pelat atap beton; tidak masuk model/kuantitas default dan belum dianalisis.

Tidak memakai image/font/library eksternal. File terpisah dari master arsitektur RevCB. Seluruh sheet berstatus rencana/studi, bukan as-built, persetujuan perencana atau gambar siap bangun.

PEMILIK / PROYEK

RUMAH 10902

NAMA PEKERJAAN

PAKET GAMBAR RENCANA RUMAH DUA LANTAI

ALAMAT / TAPAK

Babat Jerawat, Surabaya (acuan dokumen; bukan survei)

DASAR GAMBAR

Master RevCB; skenario tinggi LT2 +3400 / atas balok atap +6800 mm.

DIGAMBAR

Studi berbantuan model. Bukan tanda tangan/pernyataan perencana.

DIPERIKSA

BELUM DIPERIKSA PERENCANA STRUKTUR

STATUS DOKUMEN

RENCANA / STUDI

BUKAN AS-BUILT

ISOMETRI MODEL / RANGKA DAN TULANGAN

KODE: V-01

SKALA: NTS | A3

LEMBAR 12 / 12

UNIT: mm | CETAK 100%

P01 | 27 OKTOBER 2026

Tidak untuk pelaksanaan konstruksi.